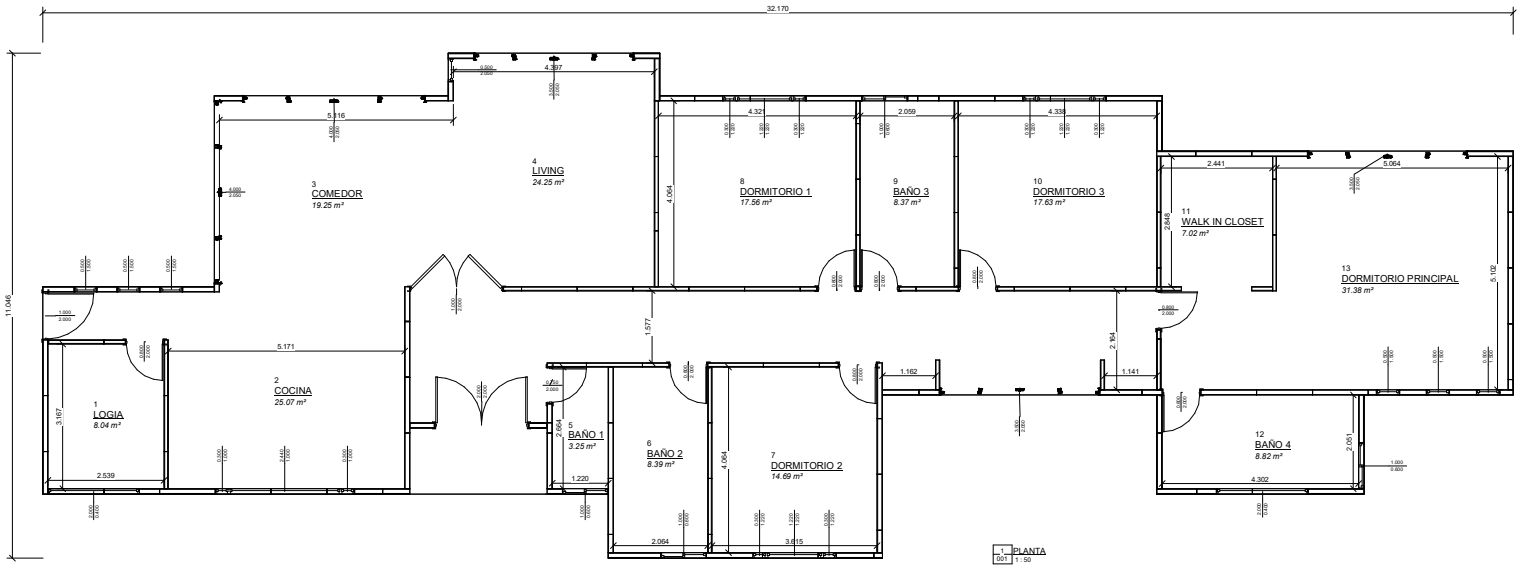

1 PLANTA
001 1 : 50

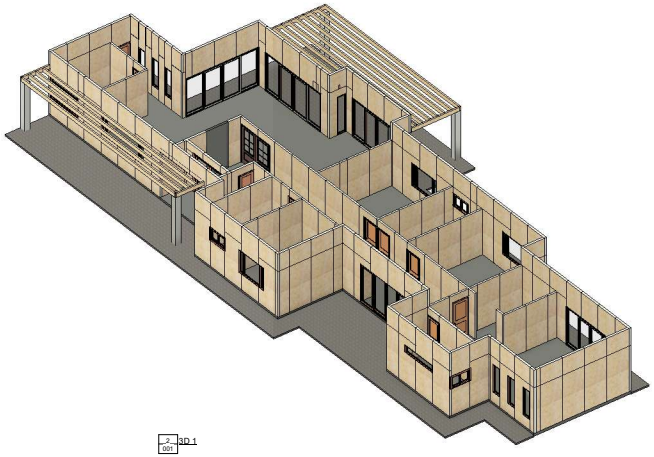

2 3D 1
001

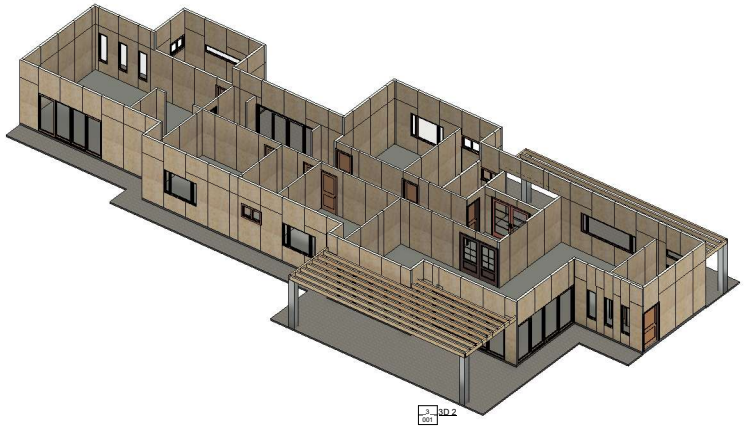

3 3D 2
001

NAPOR

1.-LOS PANELES SERAN COLOCADOS EN EL SENTIDO QUE INDIQUEN LAS FLECHAS DE SECCIÓN.

2.-LOS PANELES INTERIORES SERAN DE 90MM DE ESPESOR, MIENTRAS QUE LOS PANELES EXTERIORES SERAN DE 116MM DE ESPESOR.

Nº	Descripción	Fecha

VIVIENDA 248 m2

PROPIETARIO

NAPOR SPA.

PLANTA

Número de proyecto	19-2021
Fecha	Fecha de emisión
Dibujado por	KATTERINA GARRIDO D.
Comprobado por	Verificador
001	
Escala	1 : 50

20-11-2023 9:50:06